


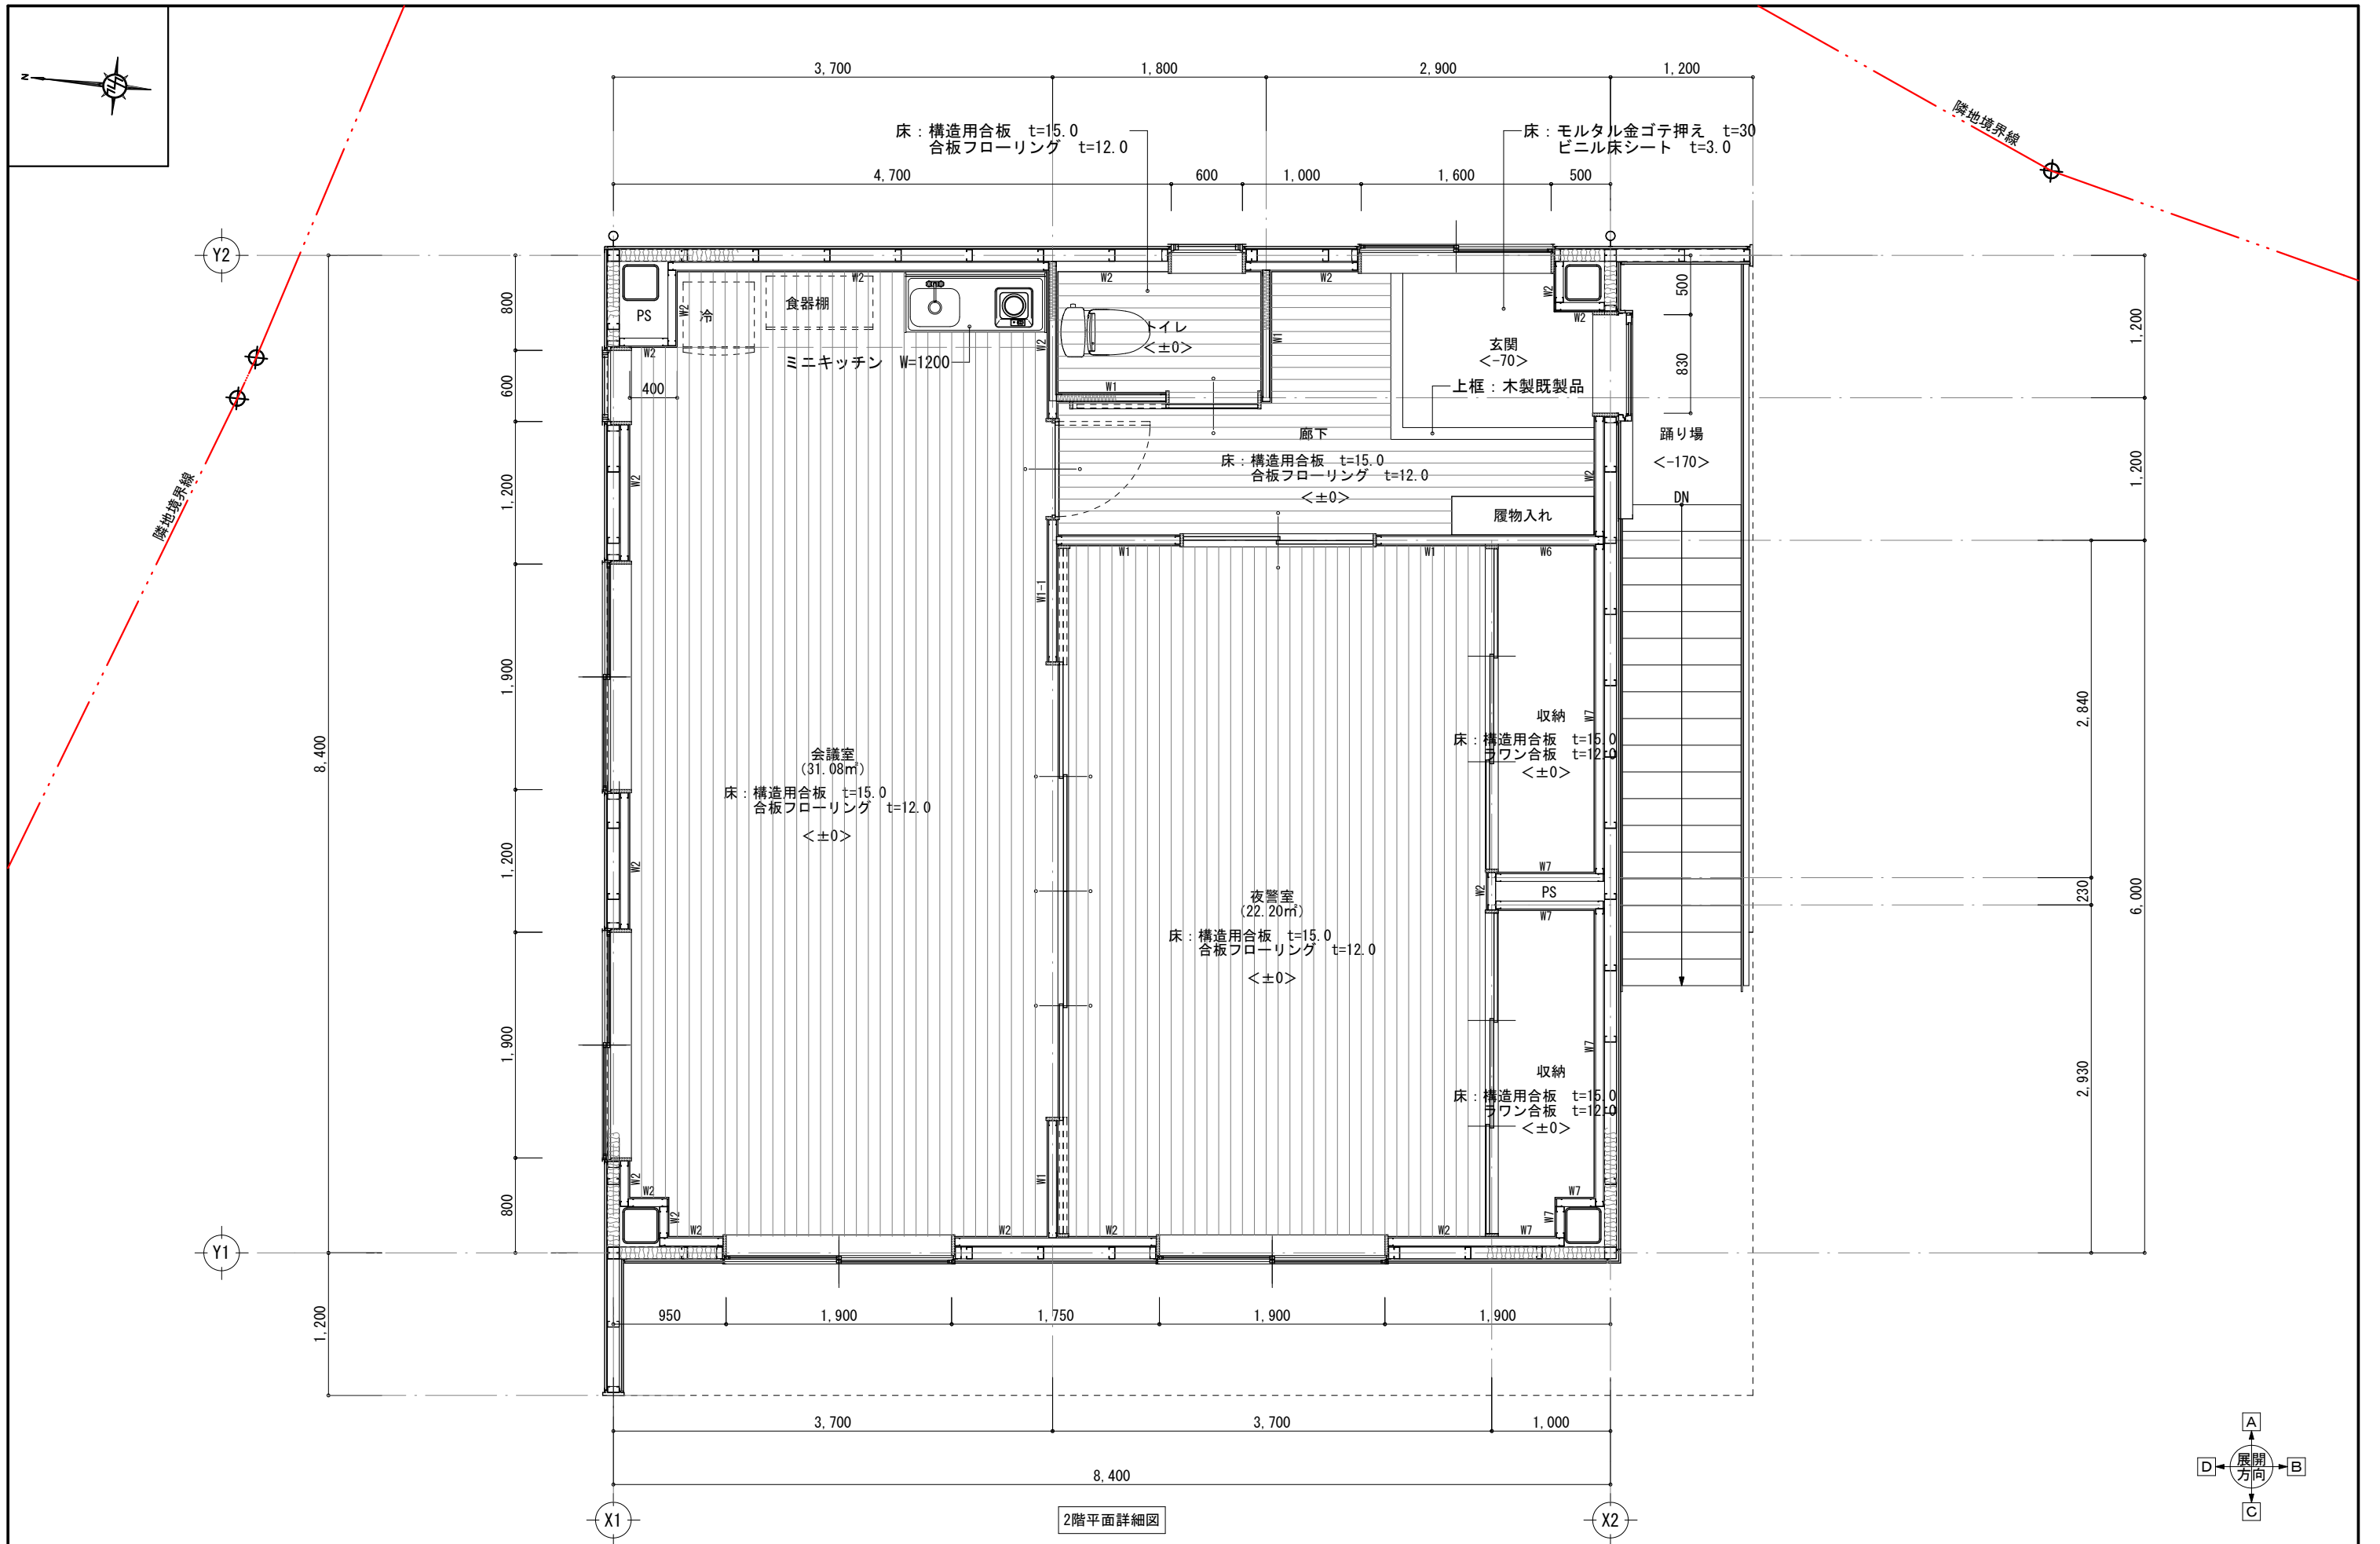

■ <※※※> 2FL±を示す



樋沢建築設計事務所

〒400-0802 山梨県甲府市横根町83-1
一級建築士事務所 登録番号 (梨) 第1-071190
一級建築士 登録 第140820 樋沢博次

SCALE
1/50 (A3)

DATE

SUBJECT
甲州市消防団勝沼分団第一部詰所新築工事

2階平面詳細図

No. D - 14